


Ⓐ Ⓑ Ⓒ

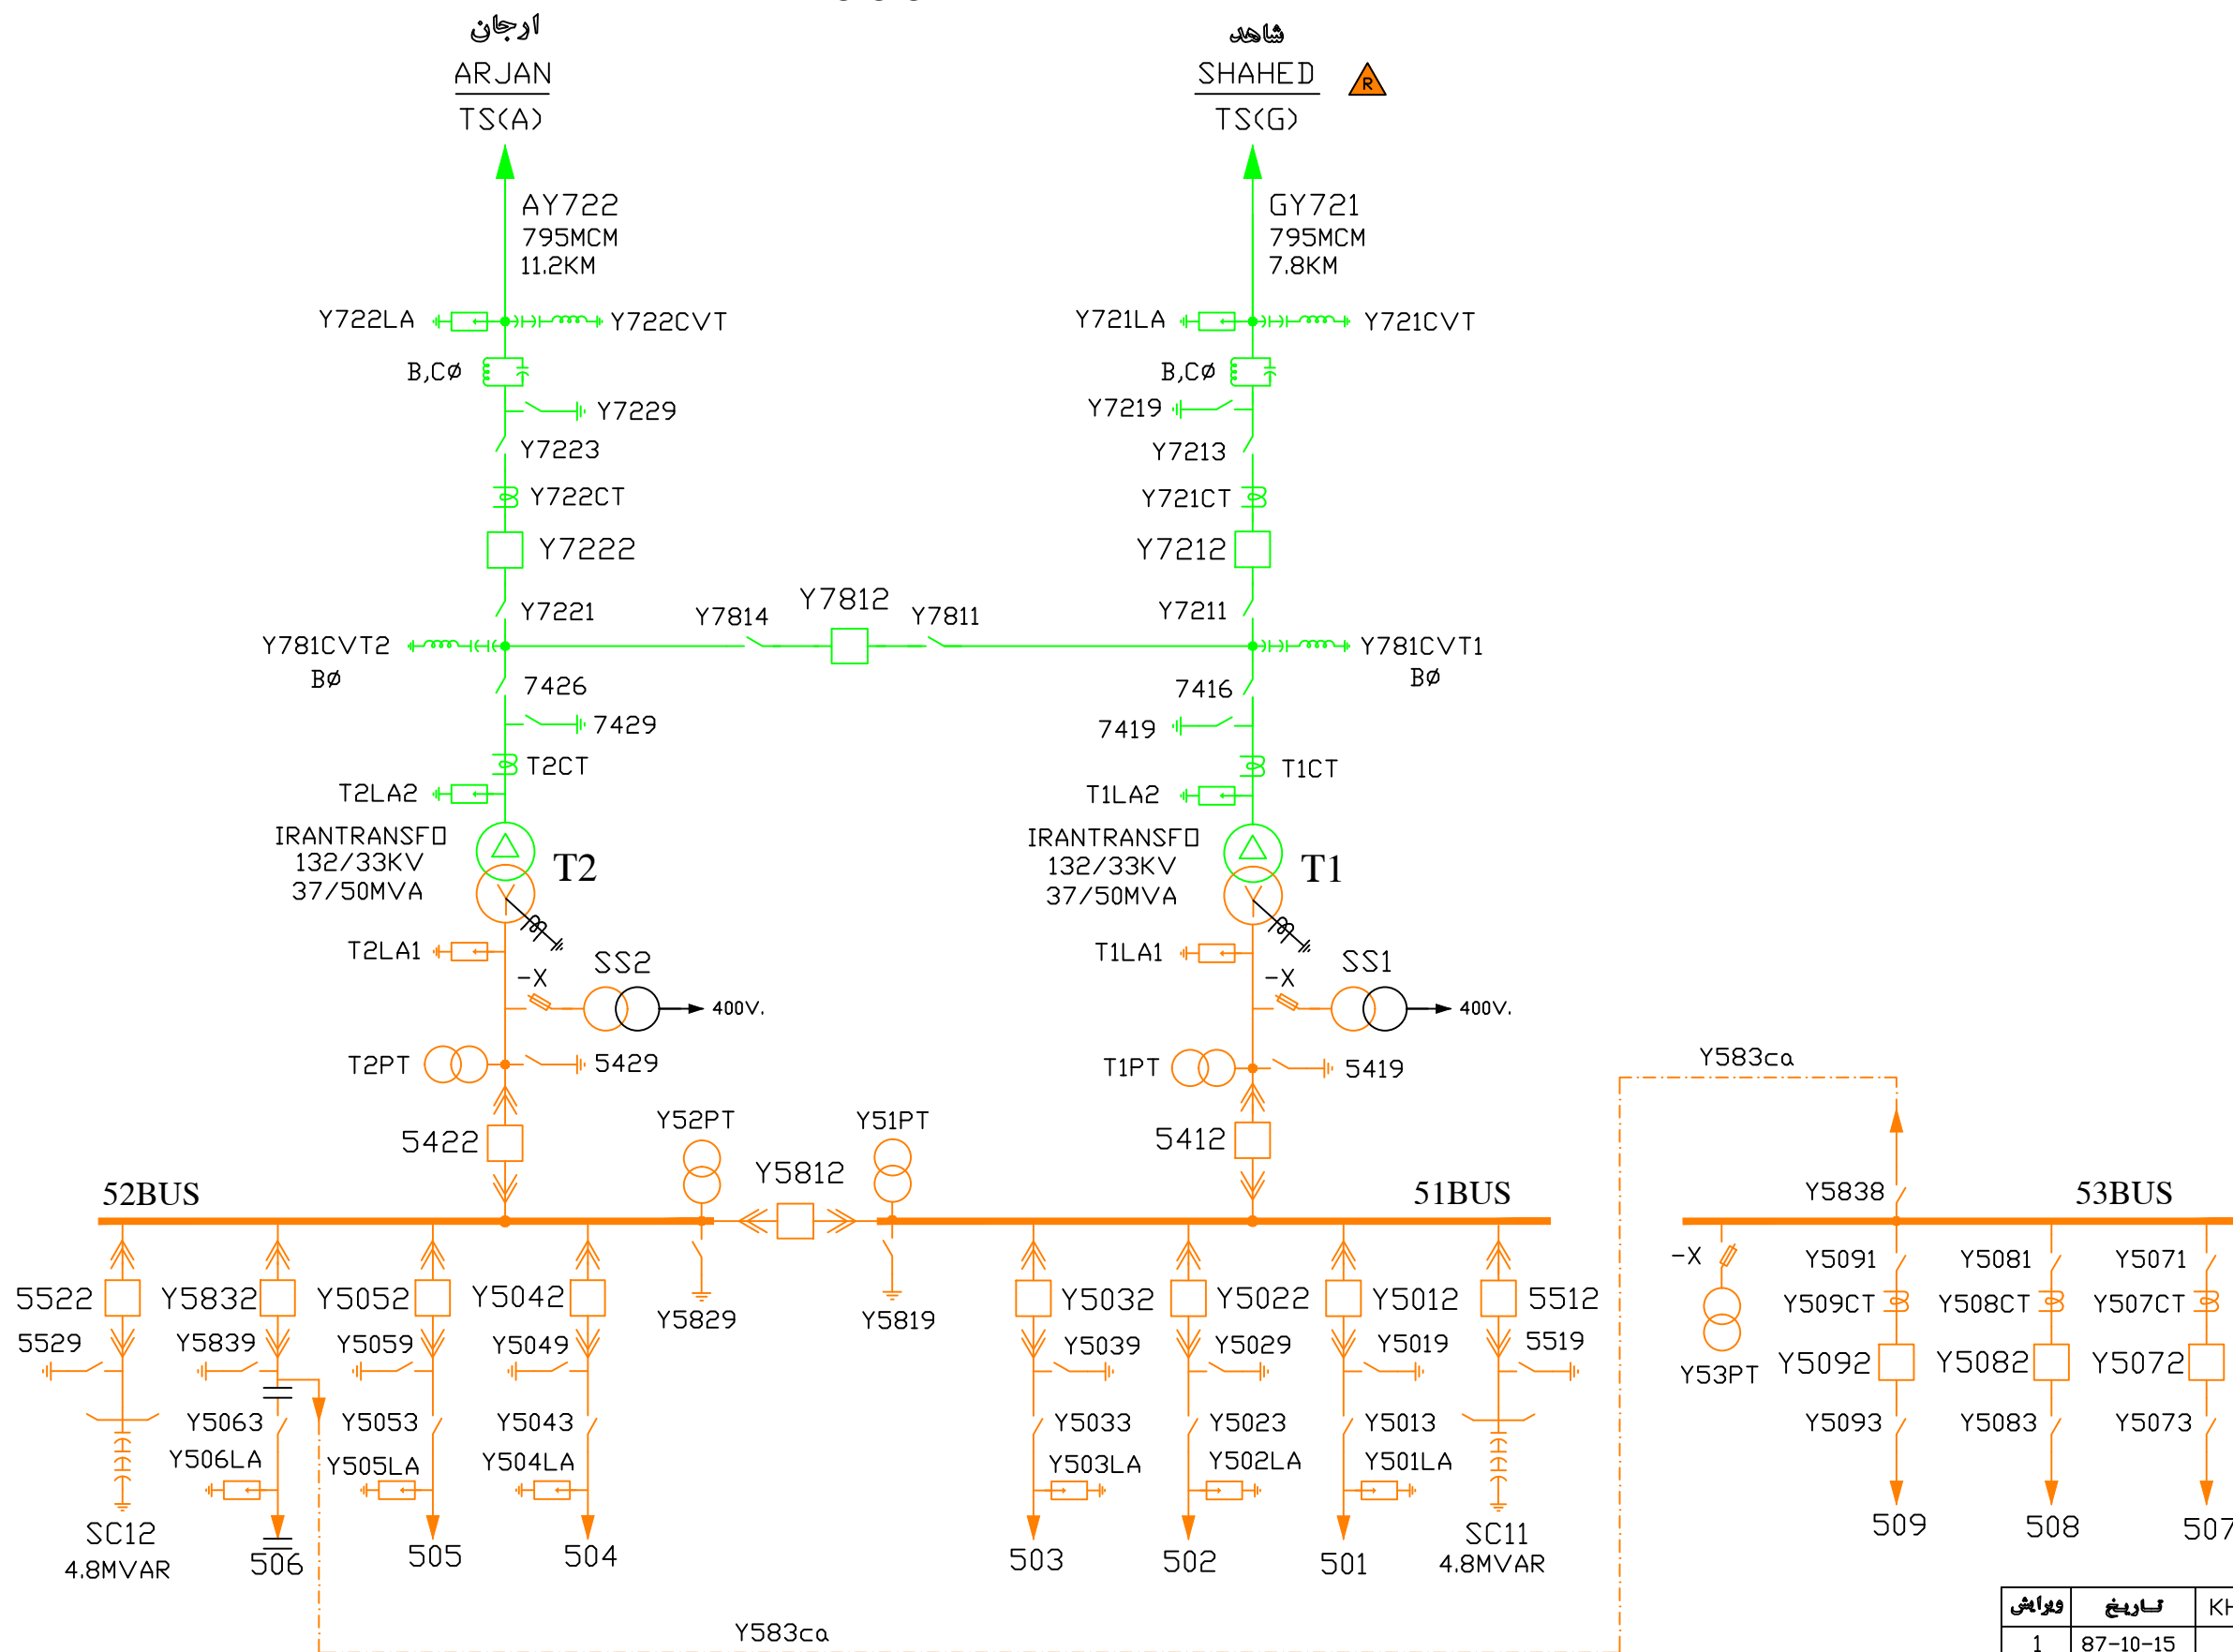

* تغییرات نسبت به ویرایش قبل

KHEIYBAR			خبر
1	87-10-15	132/33KV TS(Y)	
10	02-12-01	دیسپاچینگ منطقه جنوب غرب (SW RDC)	
11	03-02-06		
شماره نقشه	دیسپاچینگ جنوب غرب	دیسپاچینگ فوق توزیع	دیسپاچینگ جنوب غرب
SW3340	طراحی و ترسیم:	نویس:	تصویب:
بهرنگ بهادری	پیمان سلمانپور	ادیب روستایی	
صفحه 1 از 1			